Serre Rigerie

Grande serre du Bocage · implantation des tablettes

vue de dessus · échelle 1:250 (A4 paysage) · cotes en m

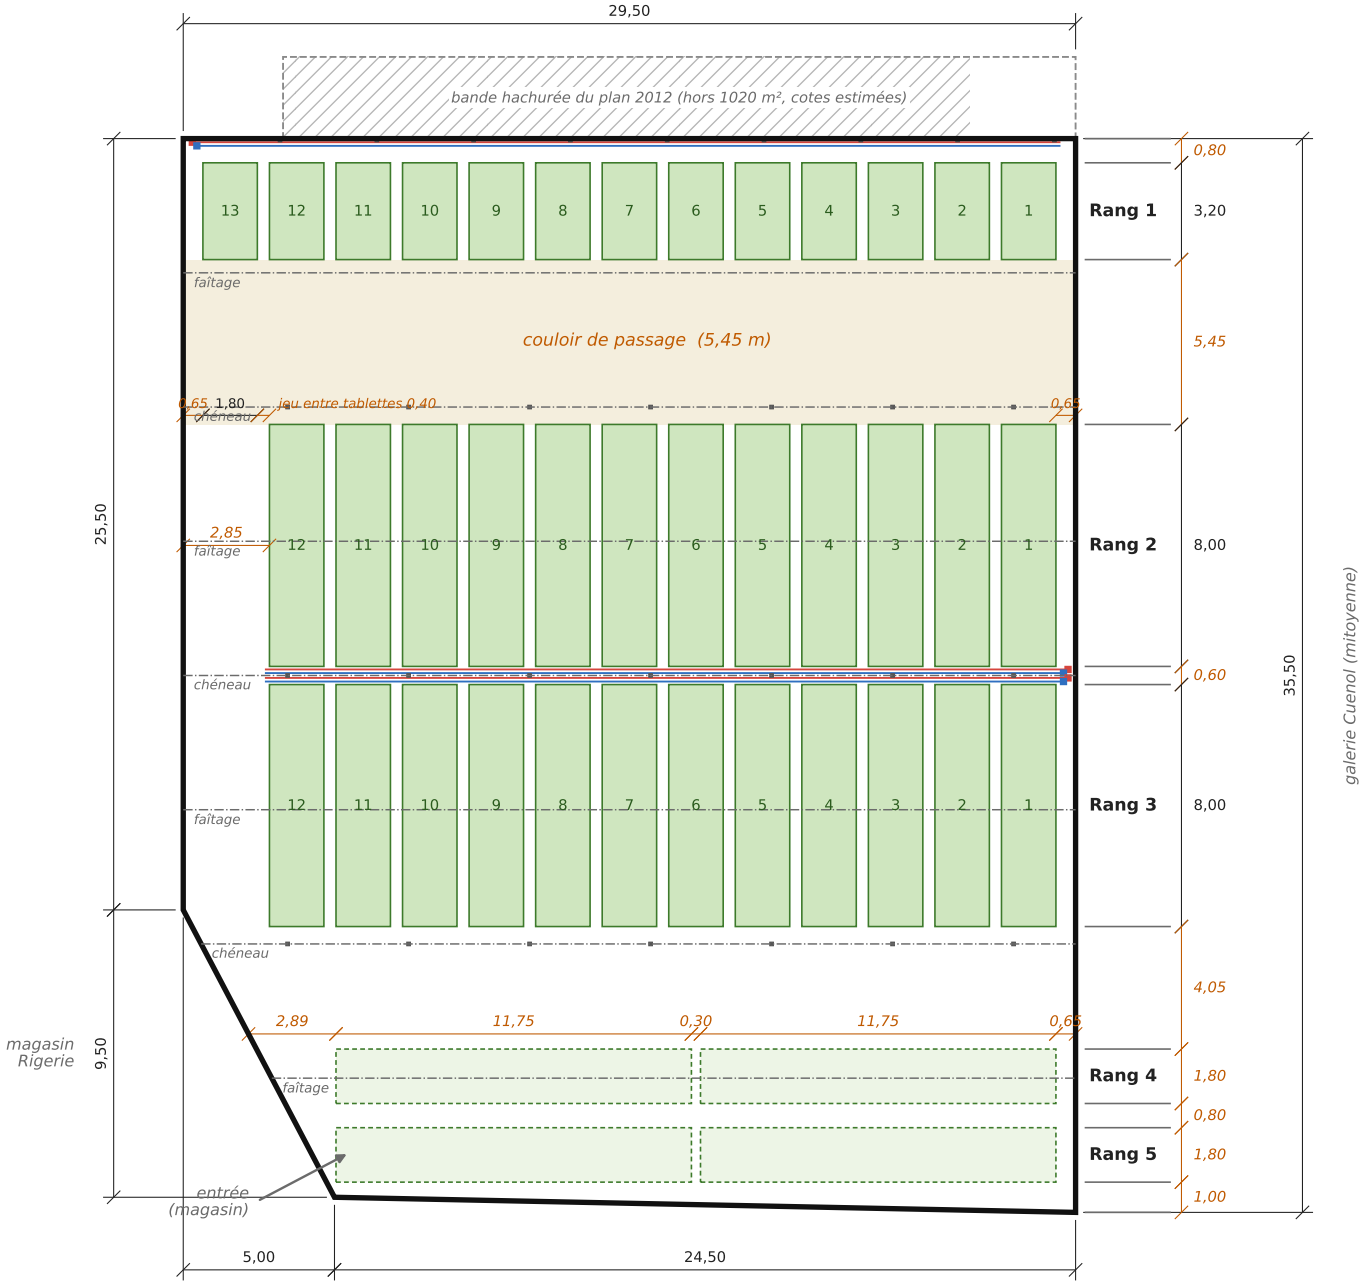

m
0 5 10

Rang	Nb	Tablette (m)	Surface	Source
1	13	1,80 × 3,20	74,9 m²	donné 22/09/2026
2	12	1,80 × 8,00	172,8 m²	donné 22/09/2026
3	12	1,80 × 8,00	172,8 m²	donné 22/09/2026
4	2	11,75 × 1,80	42,3 m²	*hyp. (rapport p.7)*
5	2	11,75 × 1,80	42,3 m²	*hyp. (rapport p.7)*
Total	**41**		**505,1 m²**	

Sol de la serre : 1015 m² calculés (1020 m² au plan 2012)
Tablettes : 50 % du sol
Toiture : 4 nefs de 8,88 m, faîtages parallèles au mur haut

Légende

- tablette, dimensions données
- tablette, dimensions supposées
- couloir de passage
- faîtage / chéneau
- tube chaud (départ), vert à 1,50 m
- tube froid (reçoit le retour), vert à 1,35 m
- poteau portant les tubes (chaînes)
- cote donnée (plan 2012, relevé du 22/09/2026)
- cote supposée, à mesurer sur place

Enveloppe : plan de site du 12/12/2012 (29,50 · 25,50 · 35,5 ; mur du magasin 5,00 × 9,50). Tablettes des rangs 1 à 3 : données du 22/09/2026, longueur des rangs 2-3 et 4 net. Jeu entre tablettes supposé (0,40 m), rang 1 centré. Rangs 4-5, recul, couloir, allées : schéma p.7 du rapport Analyse Bocage ou valeurs courantes. Réseau chaud/froid : photos du 22/09/2026 (rigerie_circu_eau/), une paire par rangée ; par tablette (rangs 1 à 3), départ chaud, retour au froid. En plan, chaque paire superposée est dédoublée pour la lisibilité. Nord non indiqué sur le plan 2012. Géométrie : bocage/plan_rigerie.py (+ DXF, CSV).